


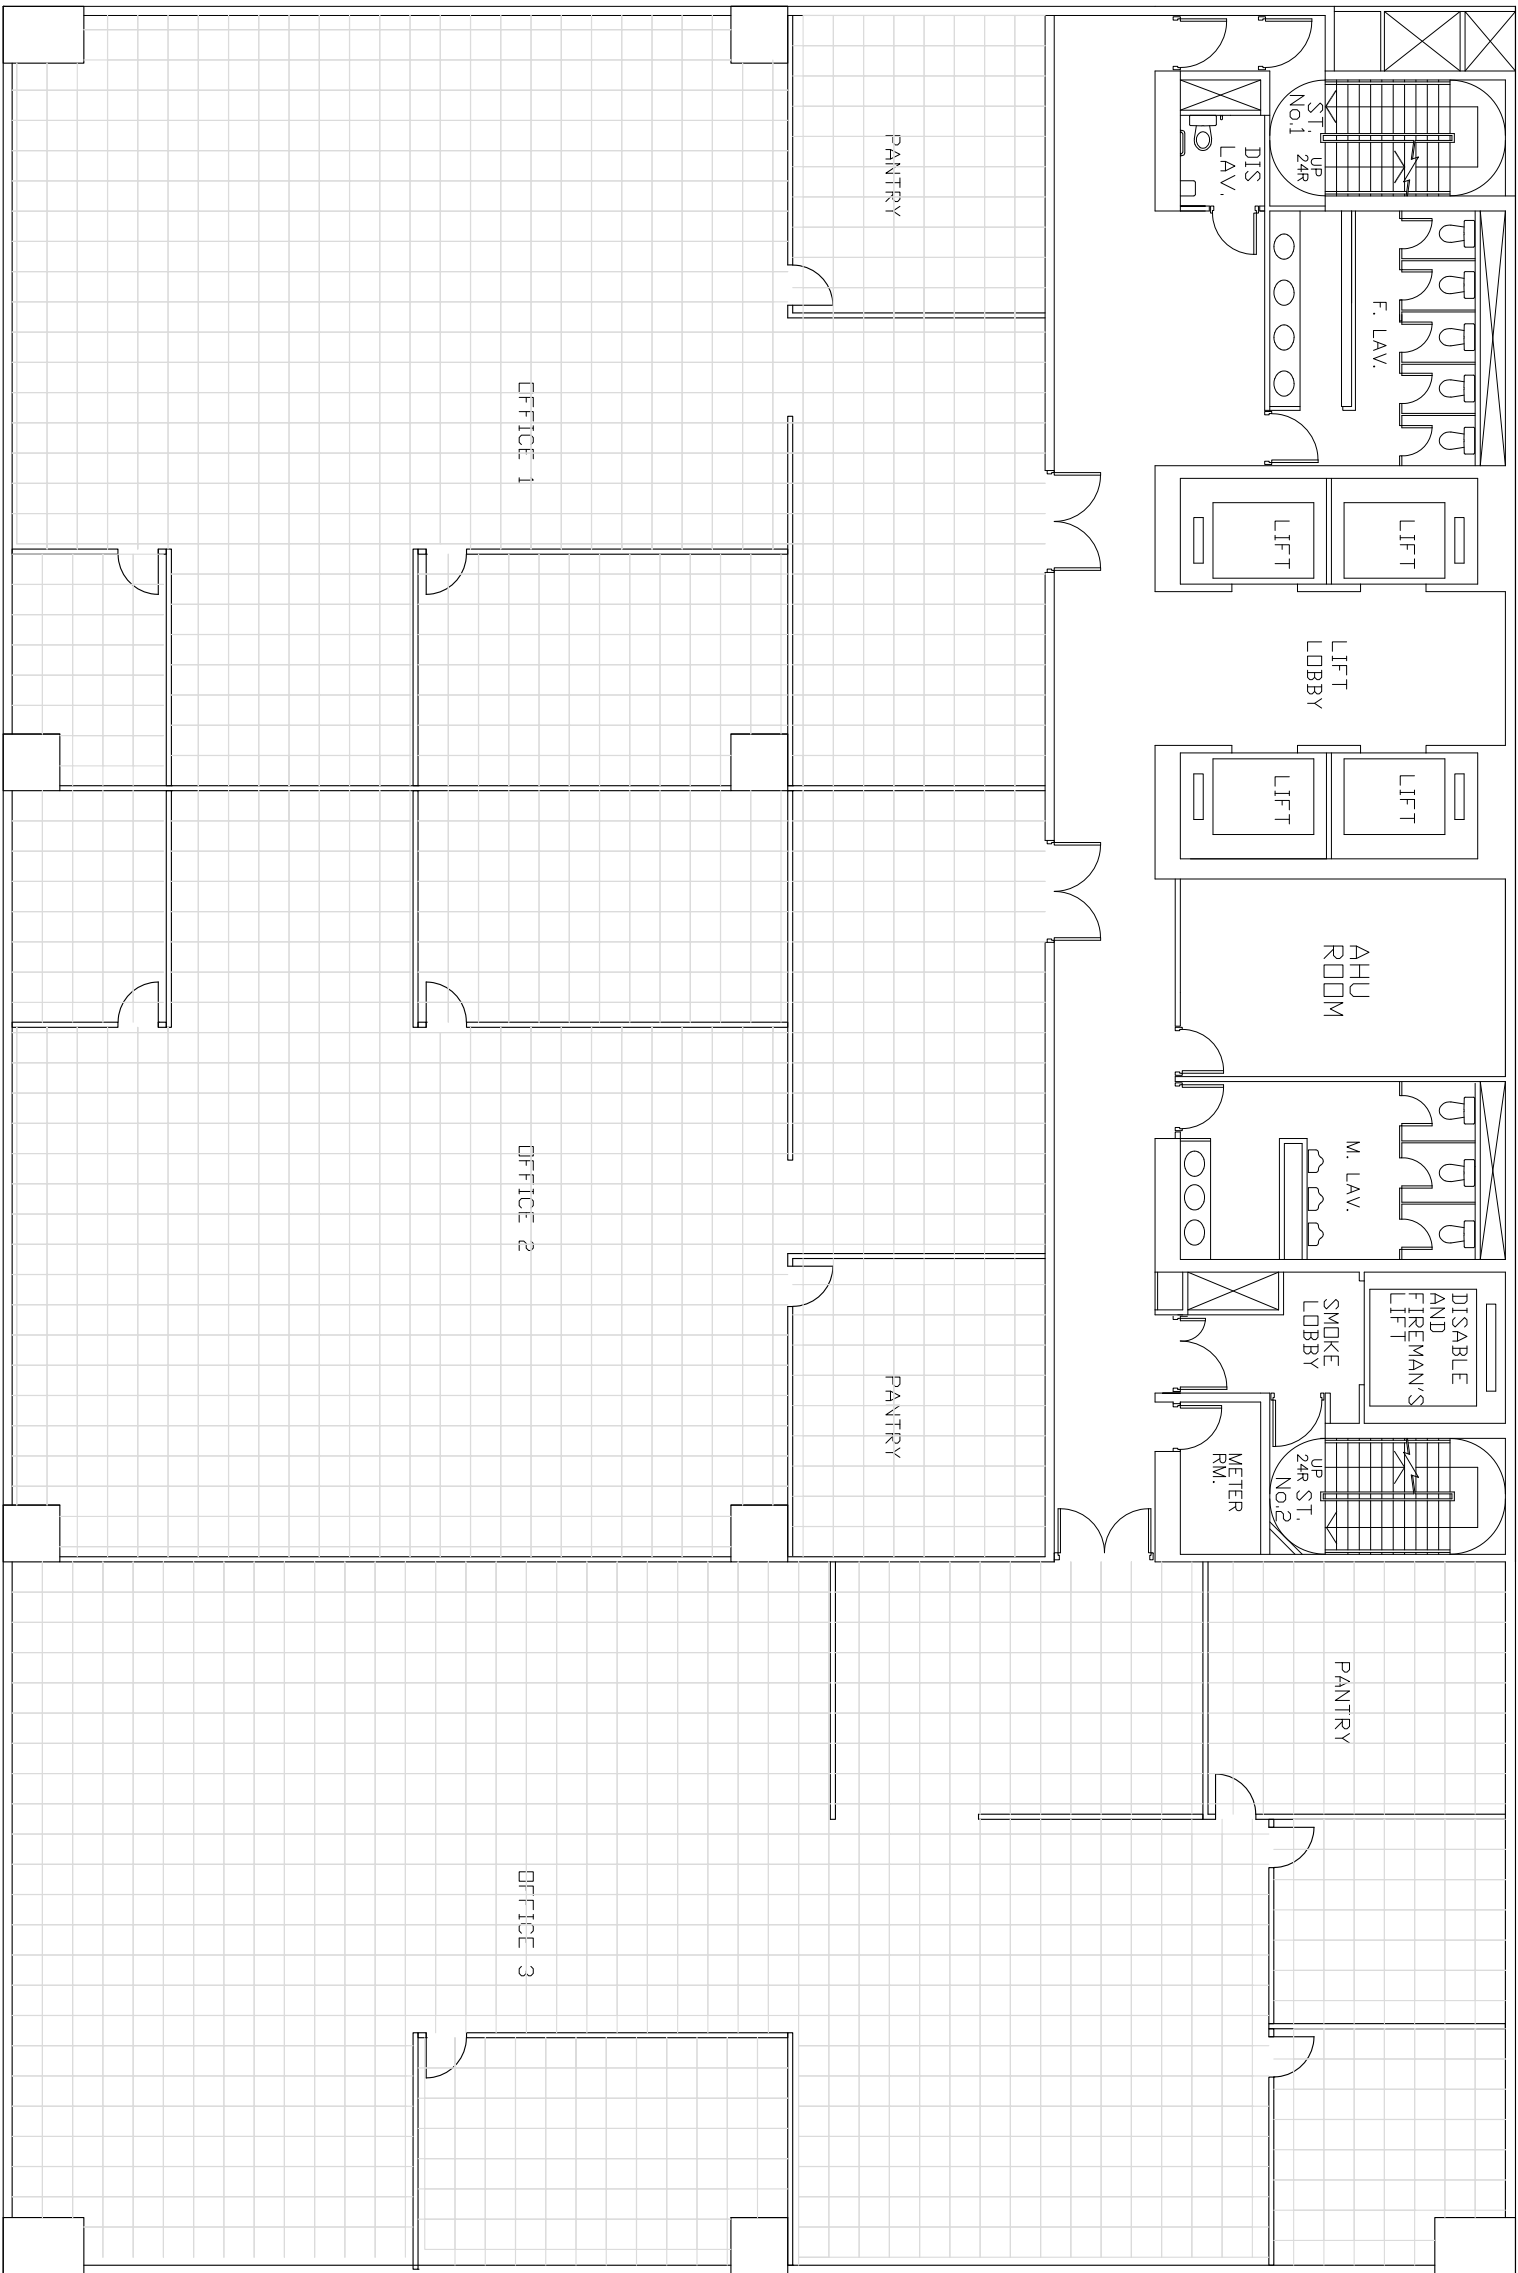

LUMINAIRE SCHEDULE

REF. NO.	SYMBOL	DESCRIPTION	LAMPS
F01		RECESSED TYPE FLUORESCENT LUMINAIRE WITH PARABOLIC REFLECTOR (SUBSCRIPT 'E' FOR FITTING C/W 2 HRS BATTERY)	3 X 14W FLUORESCENT LAMPS
F02		RECESSED TYPE DOWNLIGHT (SUBSCRIPT 'E' FOR FITTING C/W 2 HRS BATTERY)	20W COMPACT FLUORESCENT LAMP
F03		EXIT SIGN BOX C/W LUMINAIRE AND 2 HRS BATTERY	8W T5 FLUORESCENT LAMP

LIGHTING LAYOUT PLAN FOR TYPICAL FLOOR

Notes

Client

Project

Drawing

Date

Project number

Drawing number

Scale 1:150